Kerry Bruno

From:	Dan Weissman
Sent:	Friday, September 12, 2025 8:39 AM
To:	Fred Schulz
Cc:	Deanna Stockton
Subject:	FW: 86-92/94 spruce street
Attachments:	Tax Map 140.pdf

Good Morning Fred,

Do we have access to the sewer easement documents on Lot 99 in Block 30.03? This is the lot containing Barbara Boggs Sigmund Park.

Thanks,
Dan

Daniel P. Weissman
Land Use Engineer
Department of Infrastructure & Operations
Municipality of Princeton
400 Witherspoon Street | Princeton, NJ 08540
dweissman@princetonnj.gov
p: (609) 921-7077 x1251

OPEN PUBLIC RECORDS ACT NOTICE
E-mails exchanged with Princeton officials and/or employees are public records that may be subject to disclosure under the New Jersey Open Public Records Act (OPRA) N.J.SA. 47:1A-1 et seq. Although there are several exceptions to OPRAÂ¢â‚¬â„¢s disclosure requirements, there should be no expectation that the contents of the e-mails or their attachments will remain private.


From: [redacted]@verizon.net>
Sent: Thursday, September 11, 2025 12:52 PM
To: Dan Weissman <dweissman@princetonnj.gov>
Cc: Attorney Chris Tarr <cst@stevenslee.com>
Subject: 86-92/94 spruce street

This email originated from outside of the organization. Do not click links or open attachments unless you recognize the sender and know the content is safe

Hi Dan,

I'm working on design for my redevelopment site on Spruce Street. I pulled up a sewer easement the town owns, along Hamilton Ave. I've attached it, highlighted in yellow. Dominick confirms there is an easement, but no sewer line in it. I was wondering if you could share the easement documents with me. Or to whom do I need to reach out to acquire the easement docs? Thanks.

Daniel Barsky

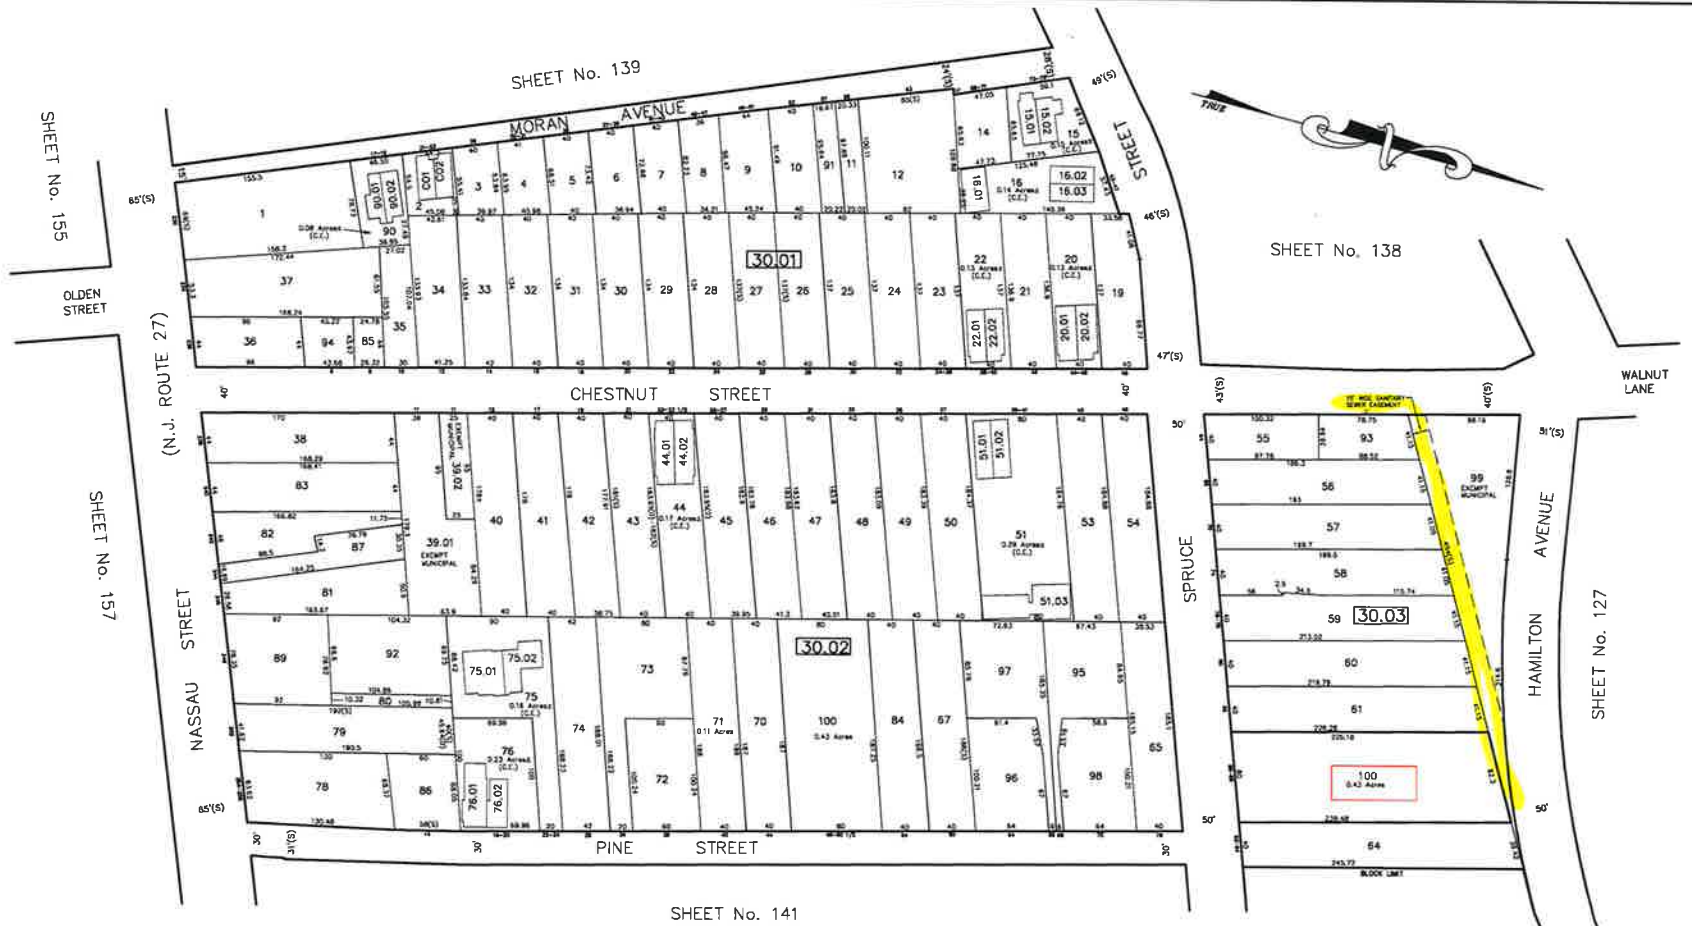

Block	Lot	Qualifier	Area	Address
30.01	2	C01	1,486 S.F.	21 MORAN AVENUE
30.01	3	C02	1,388 S.F.	23 MORAN AVENUE
30.01	15.01	C01	1,040 S.F.	72 MORAN AVENUE
30.01	15.02	C02	1,040 S.F.	73 MORAN AVENUE
30.01	16.01	C01	894 S.F.	47 SPRUCE STREET UNIT 1
30.01	16.02	C02	833 S.F.	45 SPRUCE STREET UNIT 2
30.01	16.03	C03	833 S.F.	43 SPRUCE STREET UNIT 3
30.01	20.01	C01	1,380 S.F.	44 CHESTNUT STREET
30.01	20.02	C02	1,380 S.F.	46 CHESTNUT STREET
30.01	22.01	C01	1,170 S.F.	36 CHESTNUT STREET
30.01	22.02	C02	1,170 S.F.	40 CHESTNUT STREET
30.01	90.01	C01	1,128 S.F.	17 MORAN AVENUE
30.01	90.02	C02	1,128 S.F.	19 MORAN AVENUE
30.02	44.01	C01	1,574 S.F.	23 CHESTNUT STREET
30.02	44.02	C02	1,893 S.F.	23-1/2 CHESTNUT STREET
30.02	51.01	C01	1,246 S.F.	36 CHESTNUT STREET
30.02	51.02	C02	1,292 S.F.	41 CHESTNUT STREET
30.02	51.03	C03	1,410 S.F.	41-1/2 CHESTNUT STREET
30.02	75.01	C01	1,800 S.F.	22 PINE STREET
30.02	75.02	C02	1,800 S.F.	24 PINE STREET
30.02	76.01	C01	2,030 S.F.	18 PINE STREET
30.02	76.02	C02	1,364 S.F.	20 PINE STREET

	REVISIONS	
DATE	L.S. NAME	NO.
10/1/13	GREGORY SANDUSKY	GB36756
10/31/14	GREGORY SANDUSKY	GB36756
10/1/17	GREGORY SANDUSKY	GB36756
10/1/18	GREGORY SANDUSKY	GB36756
10/1/19	GREGORY SANDUSKY	GB36756
10/1/20	GREGORY SANDUSKY	GB36756
10/1/21	GREGORY SANDUSKY	GB36756
10/1/22	GREGORY SANDUSKY	GB36756
10/1/23	GREGORY SANDUSKY	GB36756

This map has been redrawn using Computer Aided Drafting/Design (CAD/D) based on the map prepared by Kenneth R. Reiss, August, 2011.

THIS MAP SHEET HAS BEEN FORMALLY CERTIFIED FOR CONSOLIDATION ON 12/10/2012, ASSIGNED SERIAL NUMBER 1012, AND SIGNED BY SUE DAVIDSON (CTA SUPERVISING FIELD REPRESENTATIVE FOR THE STATE OF NEW JERSEY). A COPY OF THE ORIGINALLY APPROVED MAPS ARE ON FILE AT THE MUNICIPALITY OF PRINCETON LOCATED AT 400 WITHERSPOON STREET, PRINCETON, NJ. THE NEW JERSEY STATE DIVISION OF TAXATION IS RETAINING THE OFFICIAL APPOVED MAPS.

TAX MAP
PRINCETON
MERCER COUNTY, NEW JERSEY
SCALE: 1" = 50' OCTOBER, 2012
DAVID B. DIXON, PLS
Professional Land Surveyor N.J. Lic. No.27282
OMLAND ENGINEERING ASSOCIATES, INC.
CEDAR KNOLLS, NEW JERSEY
To Show Conditions as of October, 2012